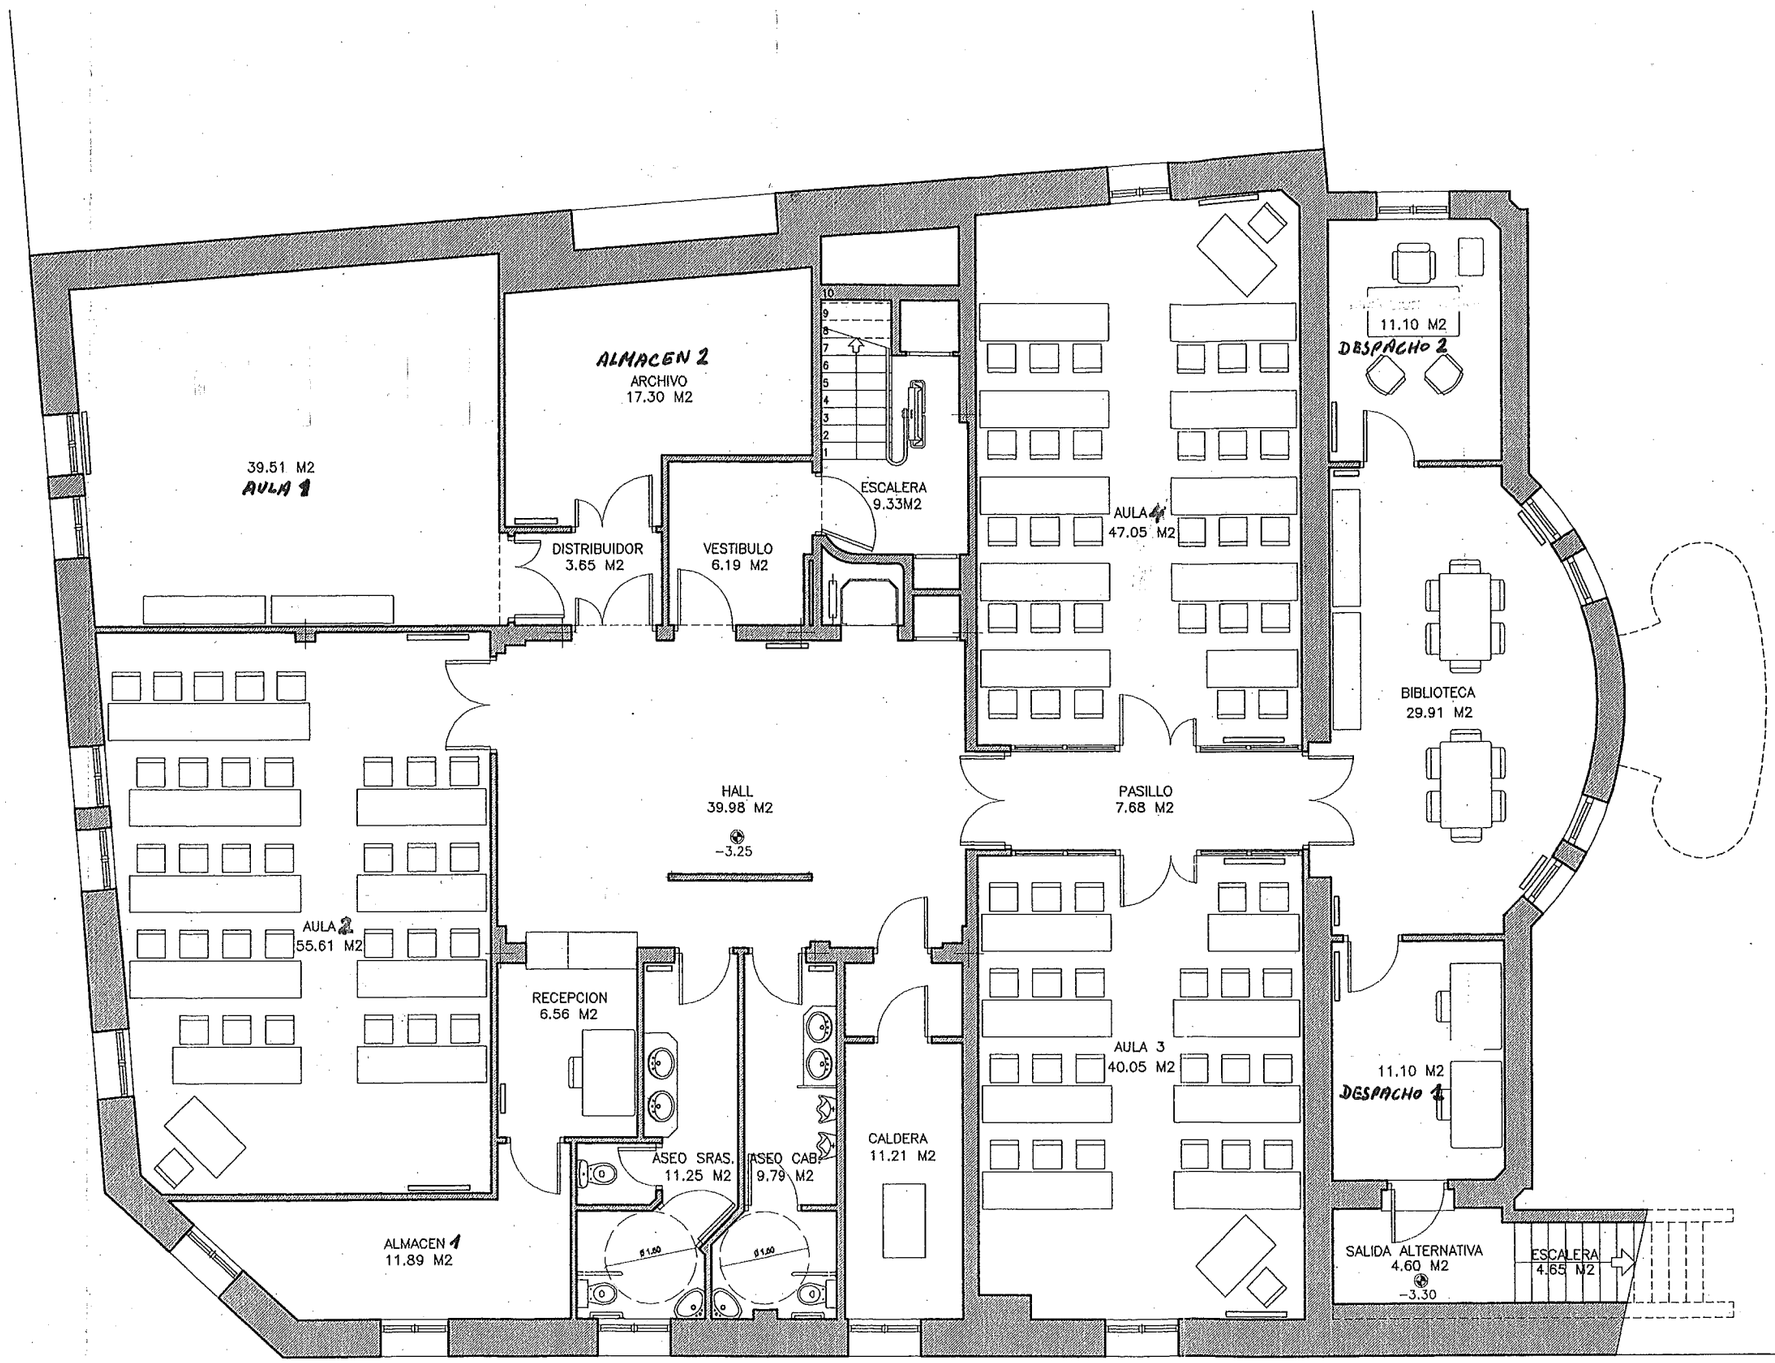

SEMISOTANO

SUP. CONSTRUIDA CERRADA	444.78 M2
SUP. CONSTRUIDA ABIERTA (SALIDA ALTERNATIVA)	11.66 M2
SUP. CONSTRUIDA TOTAL	456.44 M2
SUP. UTIL CERRADA	369.16 M2
SUP. UTIL ABIERTA (SALIDA ALTERNATIVA)	9.25 M2
SUP. UTIL TOTAL	378.41 M2

DOCUMENTACION FINAL DE OBRA
OBRAS DE REFORMA EN EL EDIFICIO SEDI
DE ESPAÑA, SITUADO EN LA CALLE GENEF

PLANO No: 2

PLANO DE: PLANTA SEMISOTANO. USOS Y SUPERFICIES

PROMOTOR: INSTITUTO DE LA INGENIERIA DE ESPAÑA

AF